


1ST STOREY

G.F.A. CALCULATION		
	G.F.A. (A)	= 352.85 m2
	G.F.A. TO BE REDUCED	= 0 m2
		PROPOSED GFA=352.85 m2

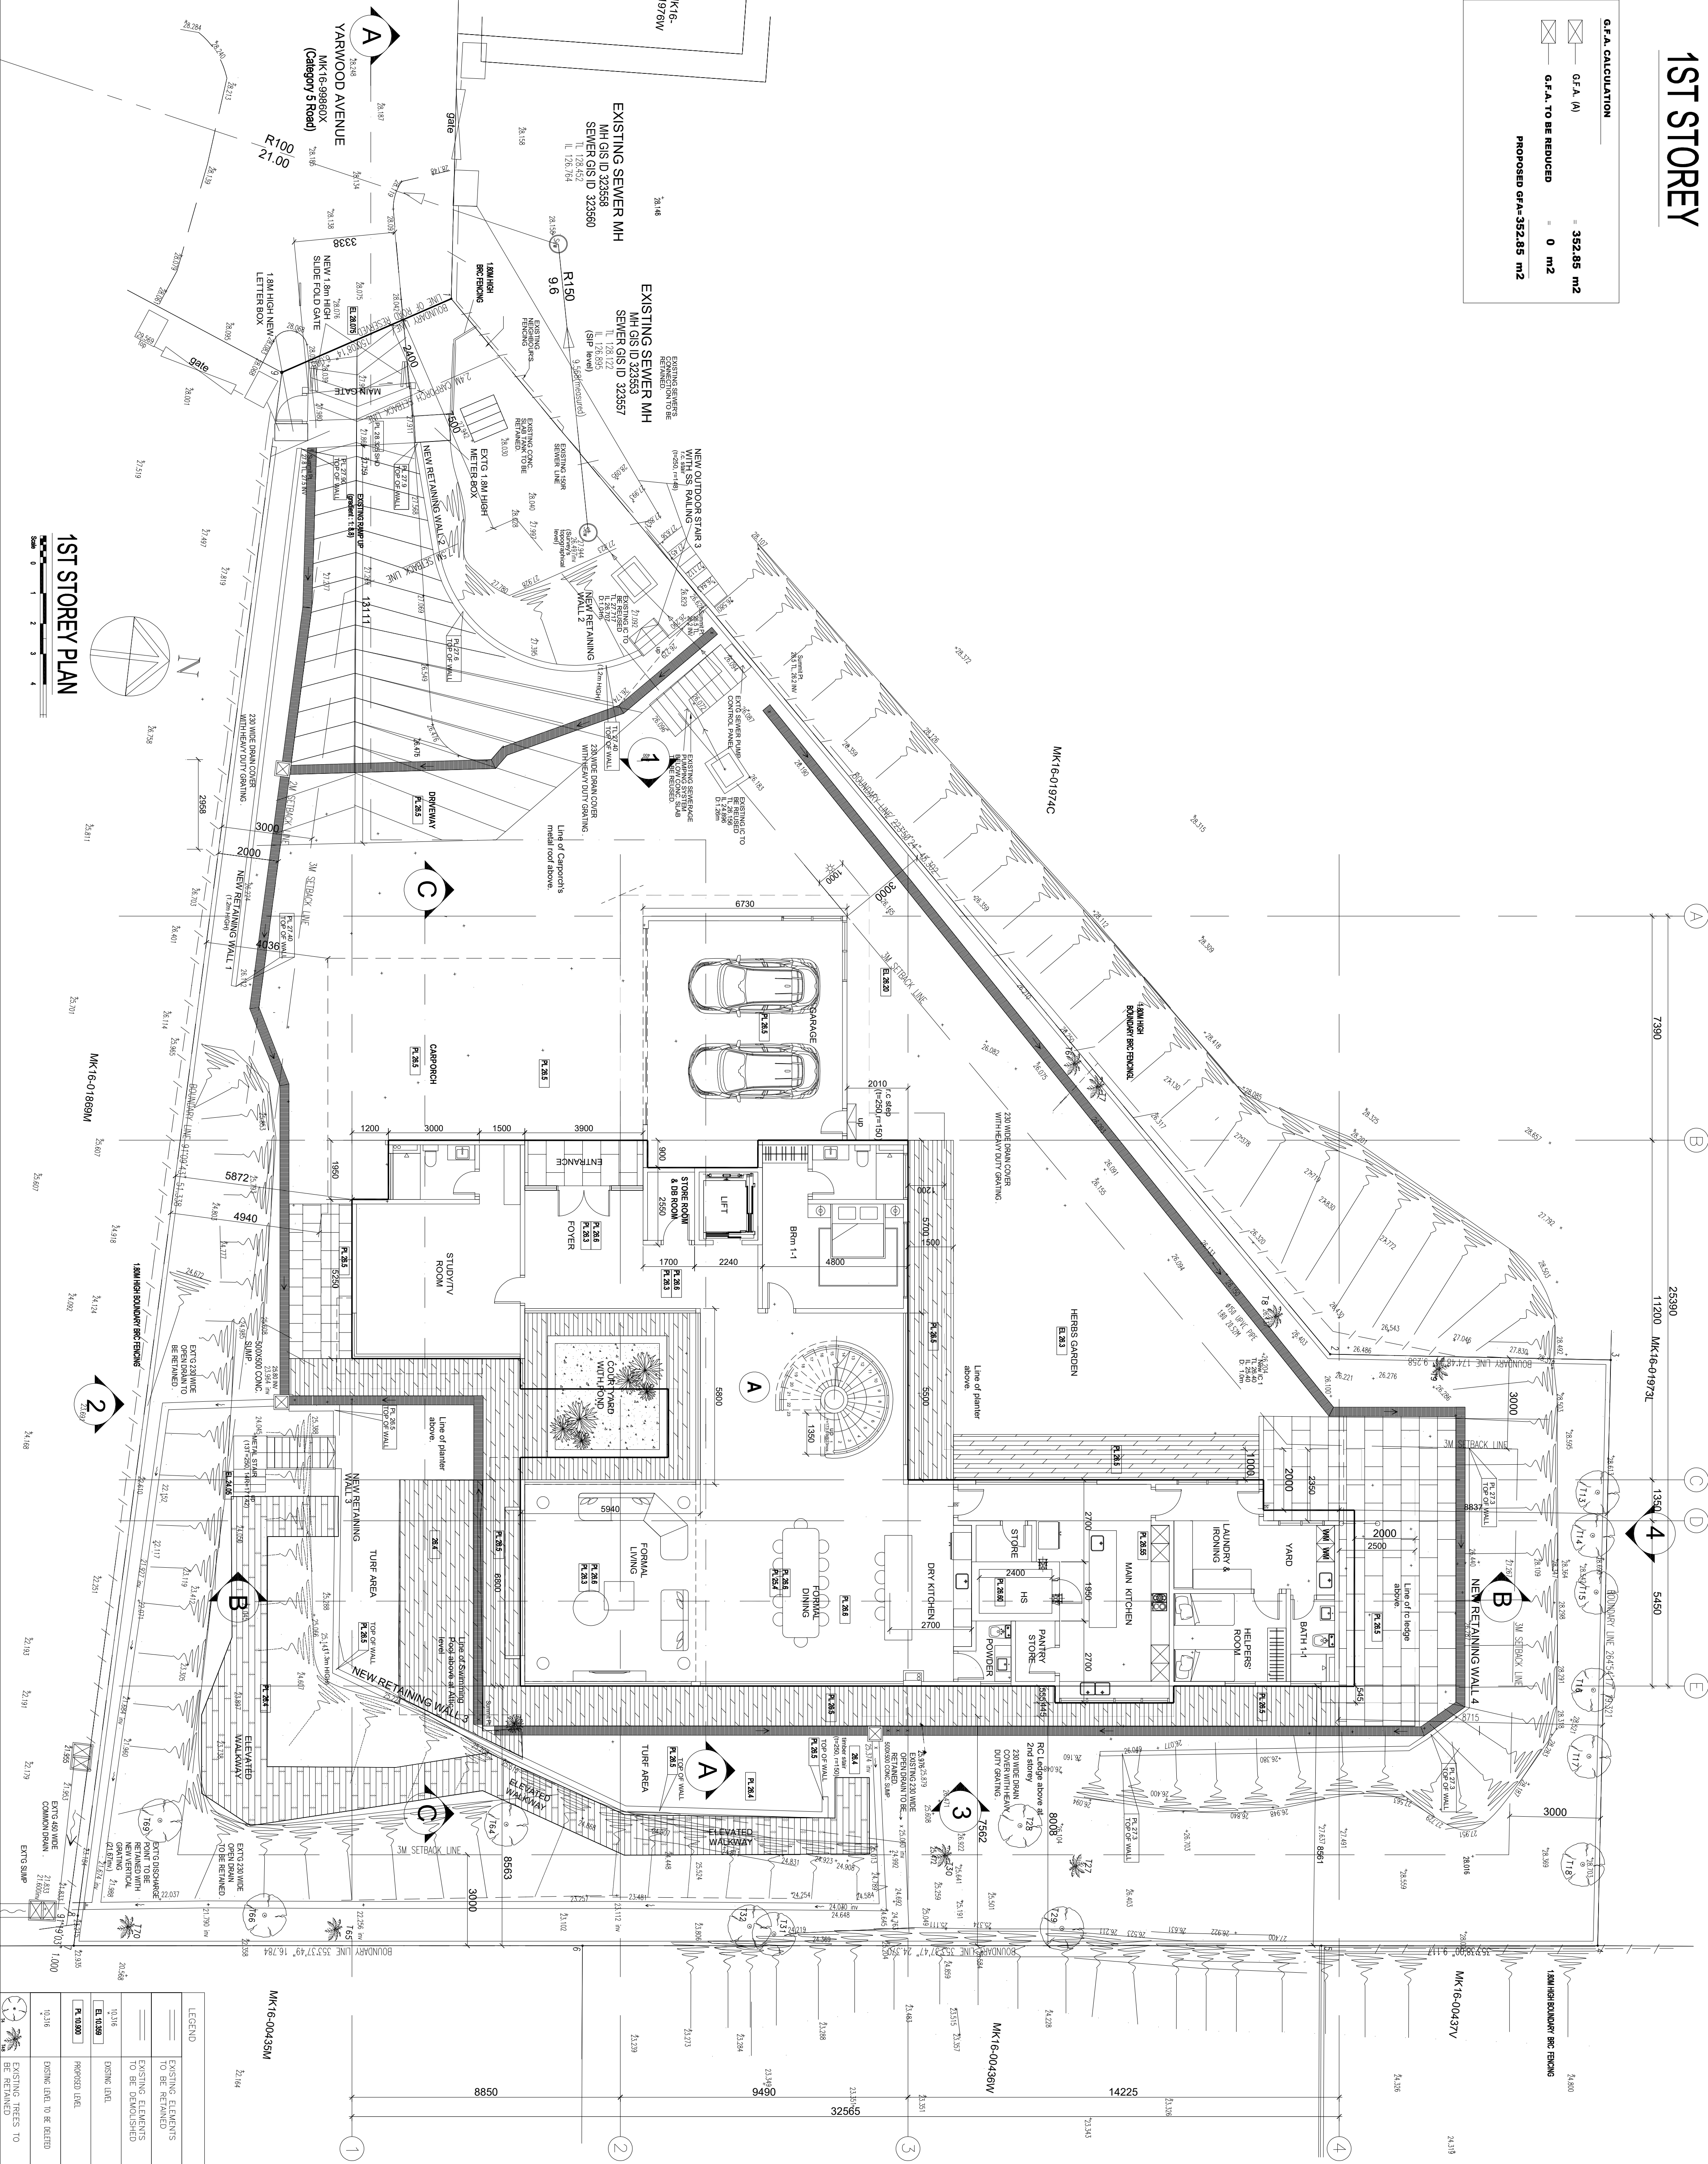

1ST STOREY PLAN

LEGEND	
	EXISTING ELEMENTS TO BE RETAINED
	EXISTING ELEMENTS TO BE DEMOLISHED
	PROPOSED LEVEL
	EXISTING TREES TO BE RETAINED