


2ND STOREY

G.F.A. CALCULATION		
	G.F.A. (B)	= 387.80 m2
	G.F.A. TO BE REDUCED (v1)	= 4.36 m2
	(v2)	= 11.06 m2
	(v3)	= 36.68 m2
	PROPOSED GFA	335.70 m2

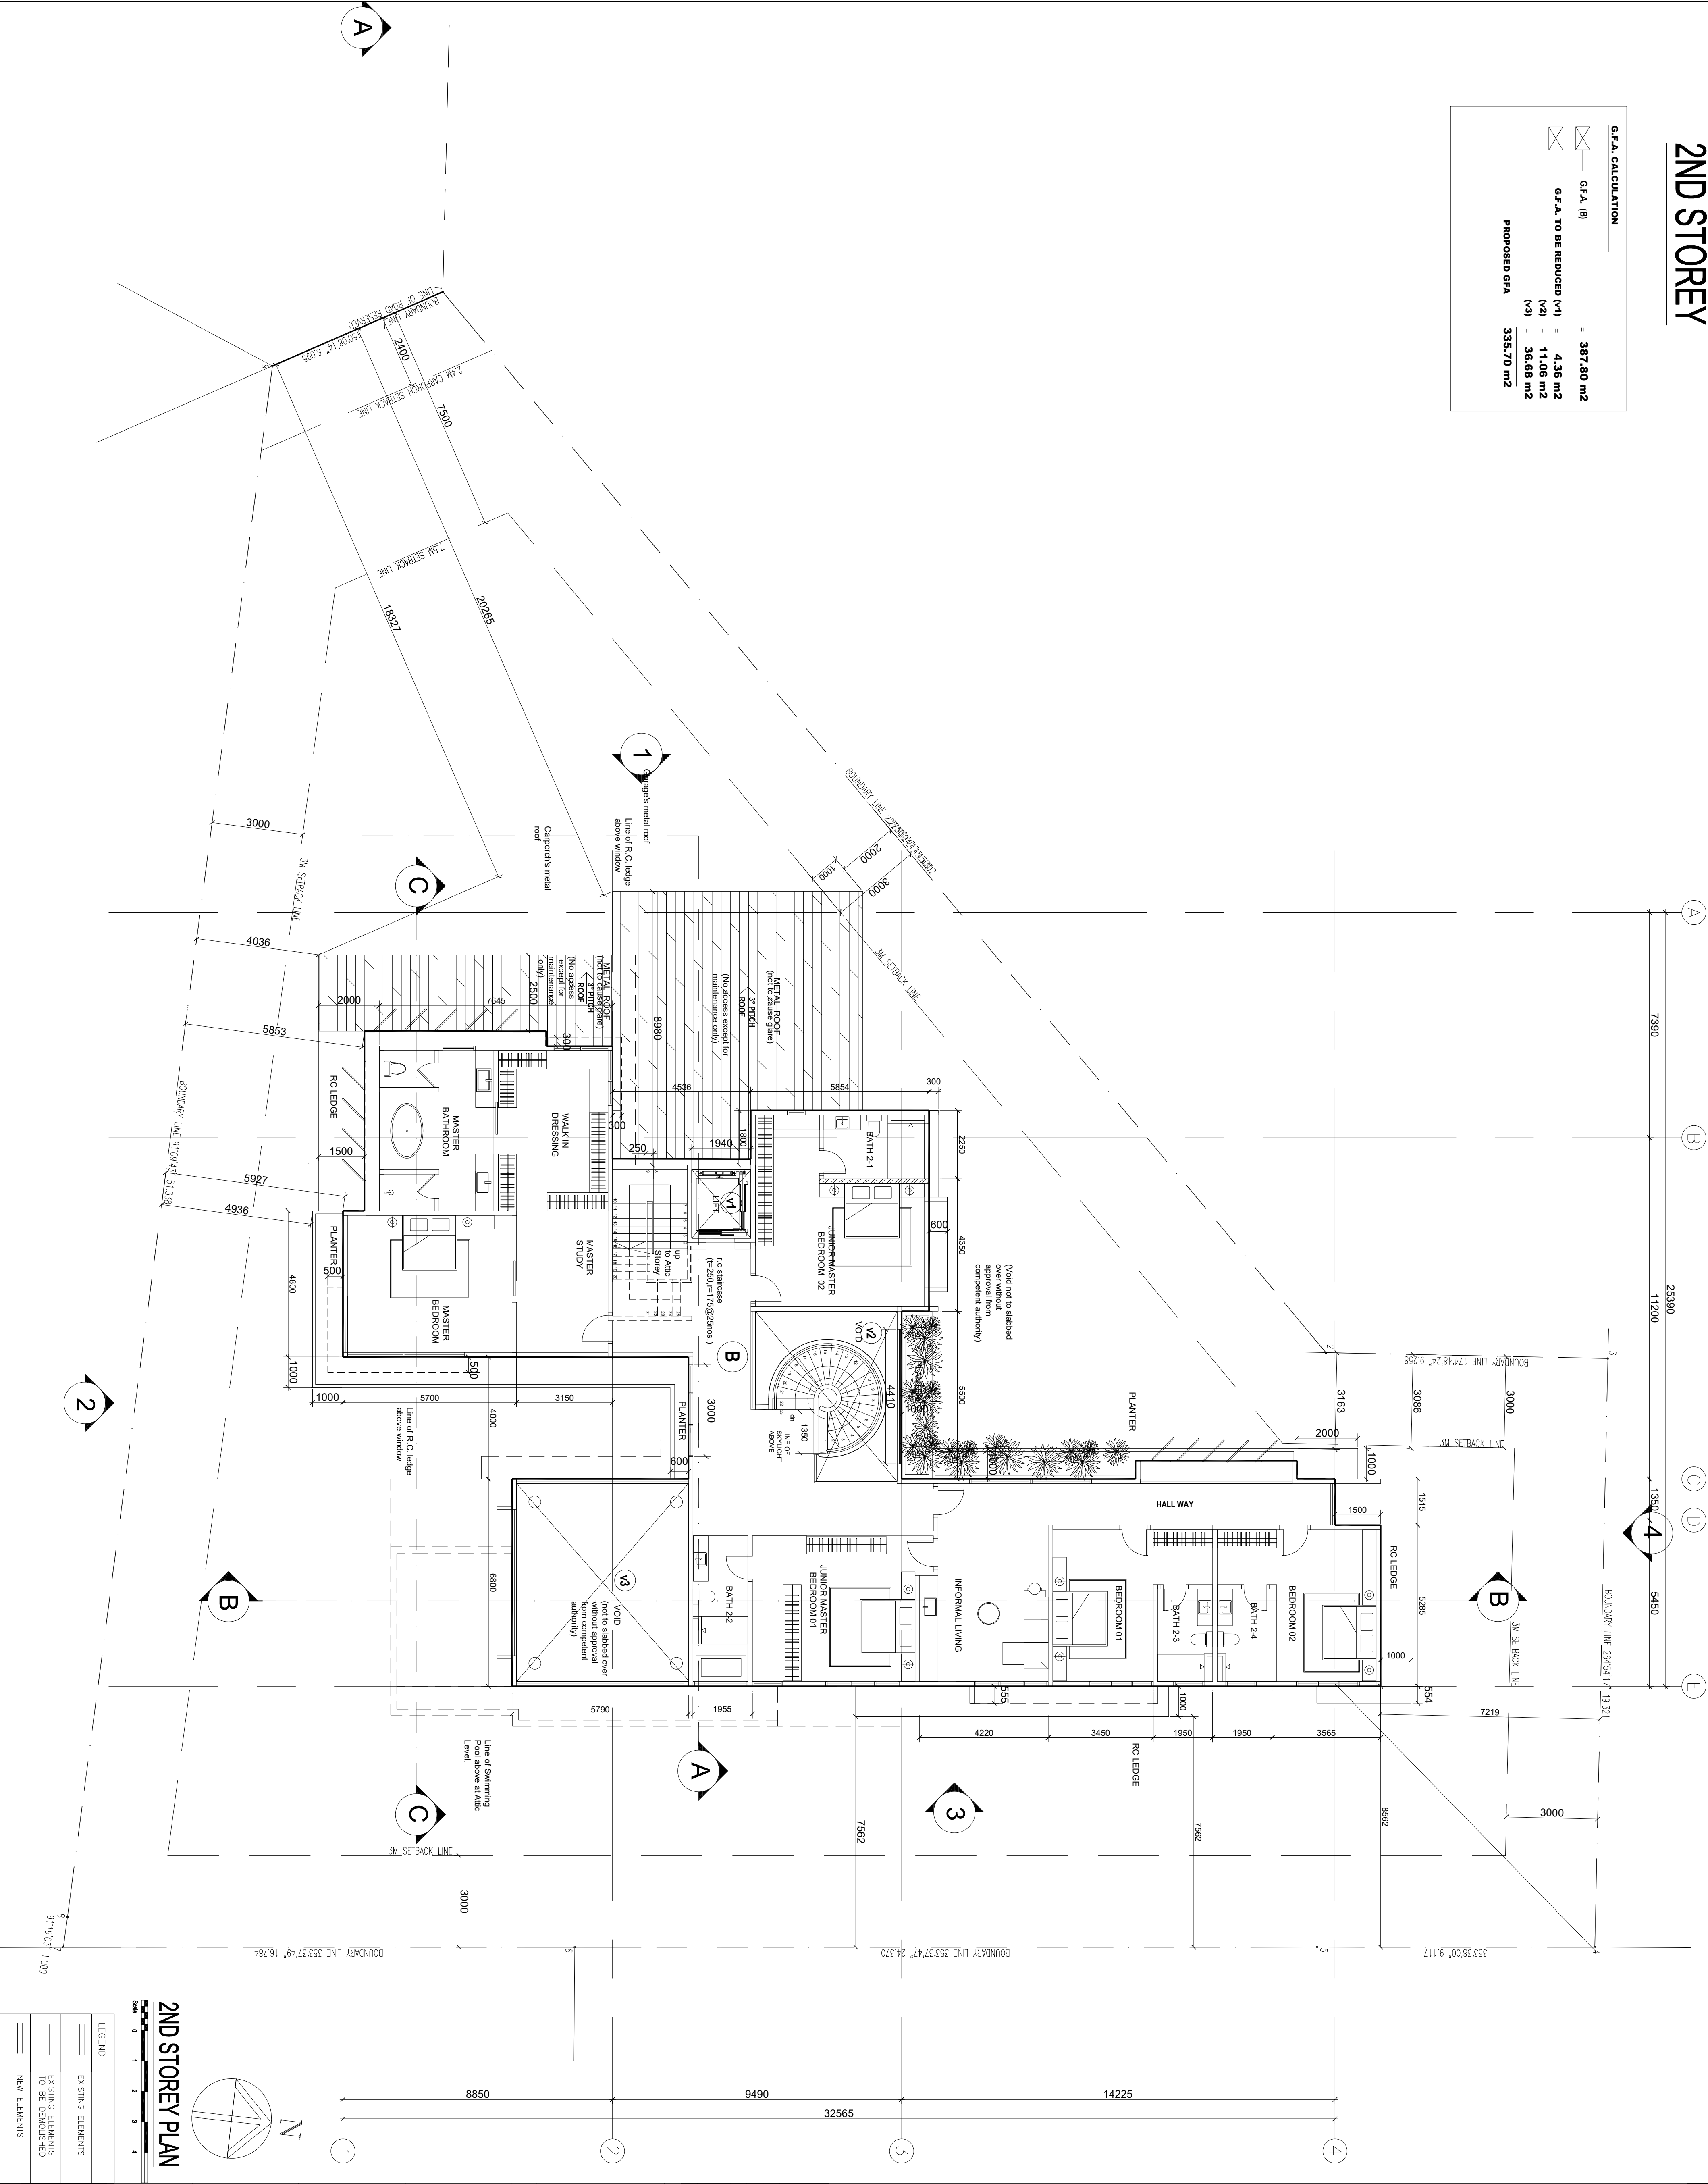

2ND STOREY PLAN

Scale 0 1 2 3 4

1:200

9°11'19.03"

16°7'8.4"

35°33'37.49"

35°33'37.47"

35°33'38.00"

9°11'17"

LEGEND

	EXISTING ELEMENTS
	EXISTING ELEMENTS TO BE DEMOLISHED
	NEW ELEMENTS