


STUDY SET NOT FOR CONSTRUCTION

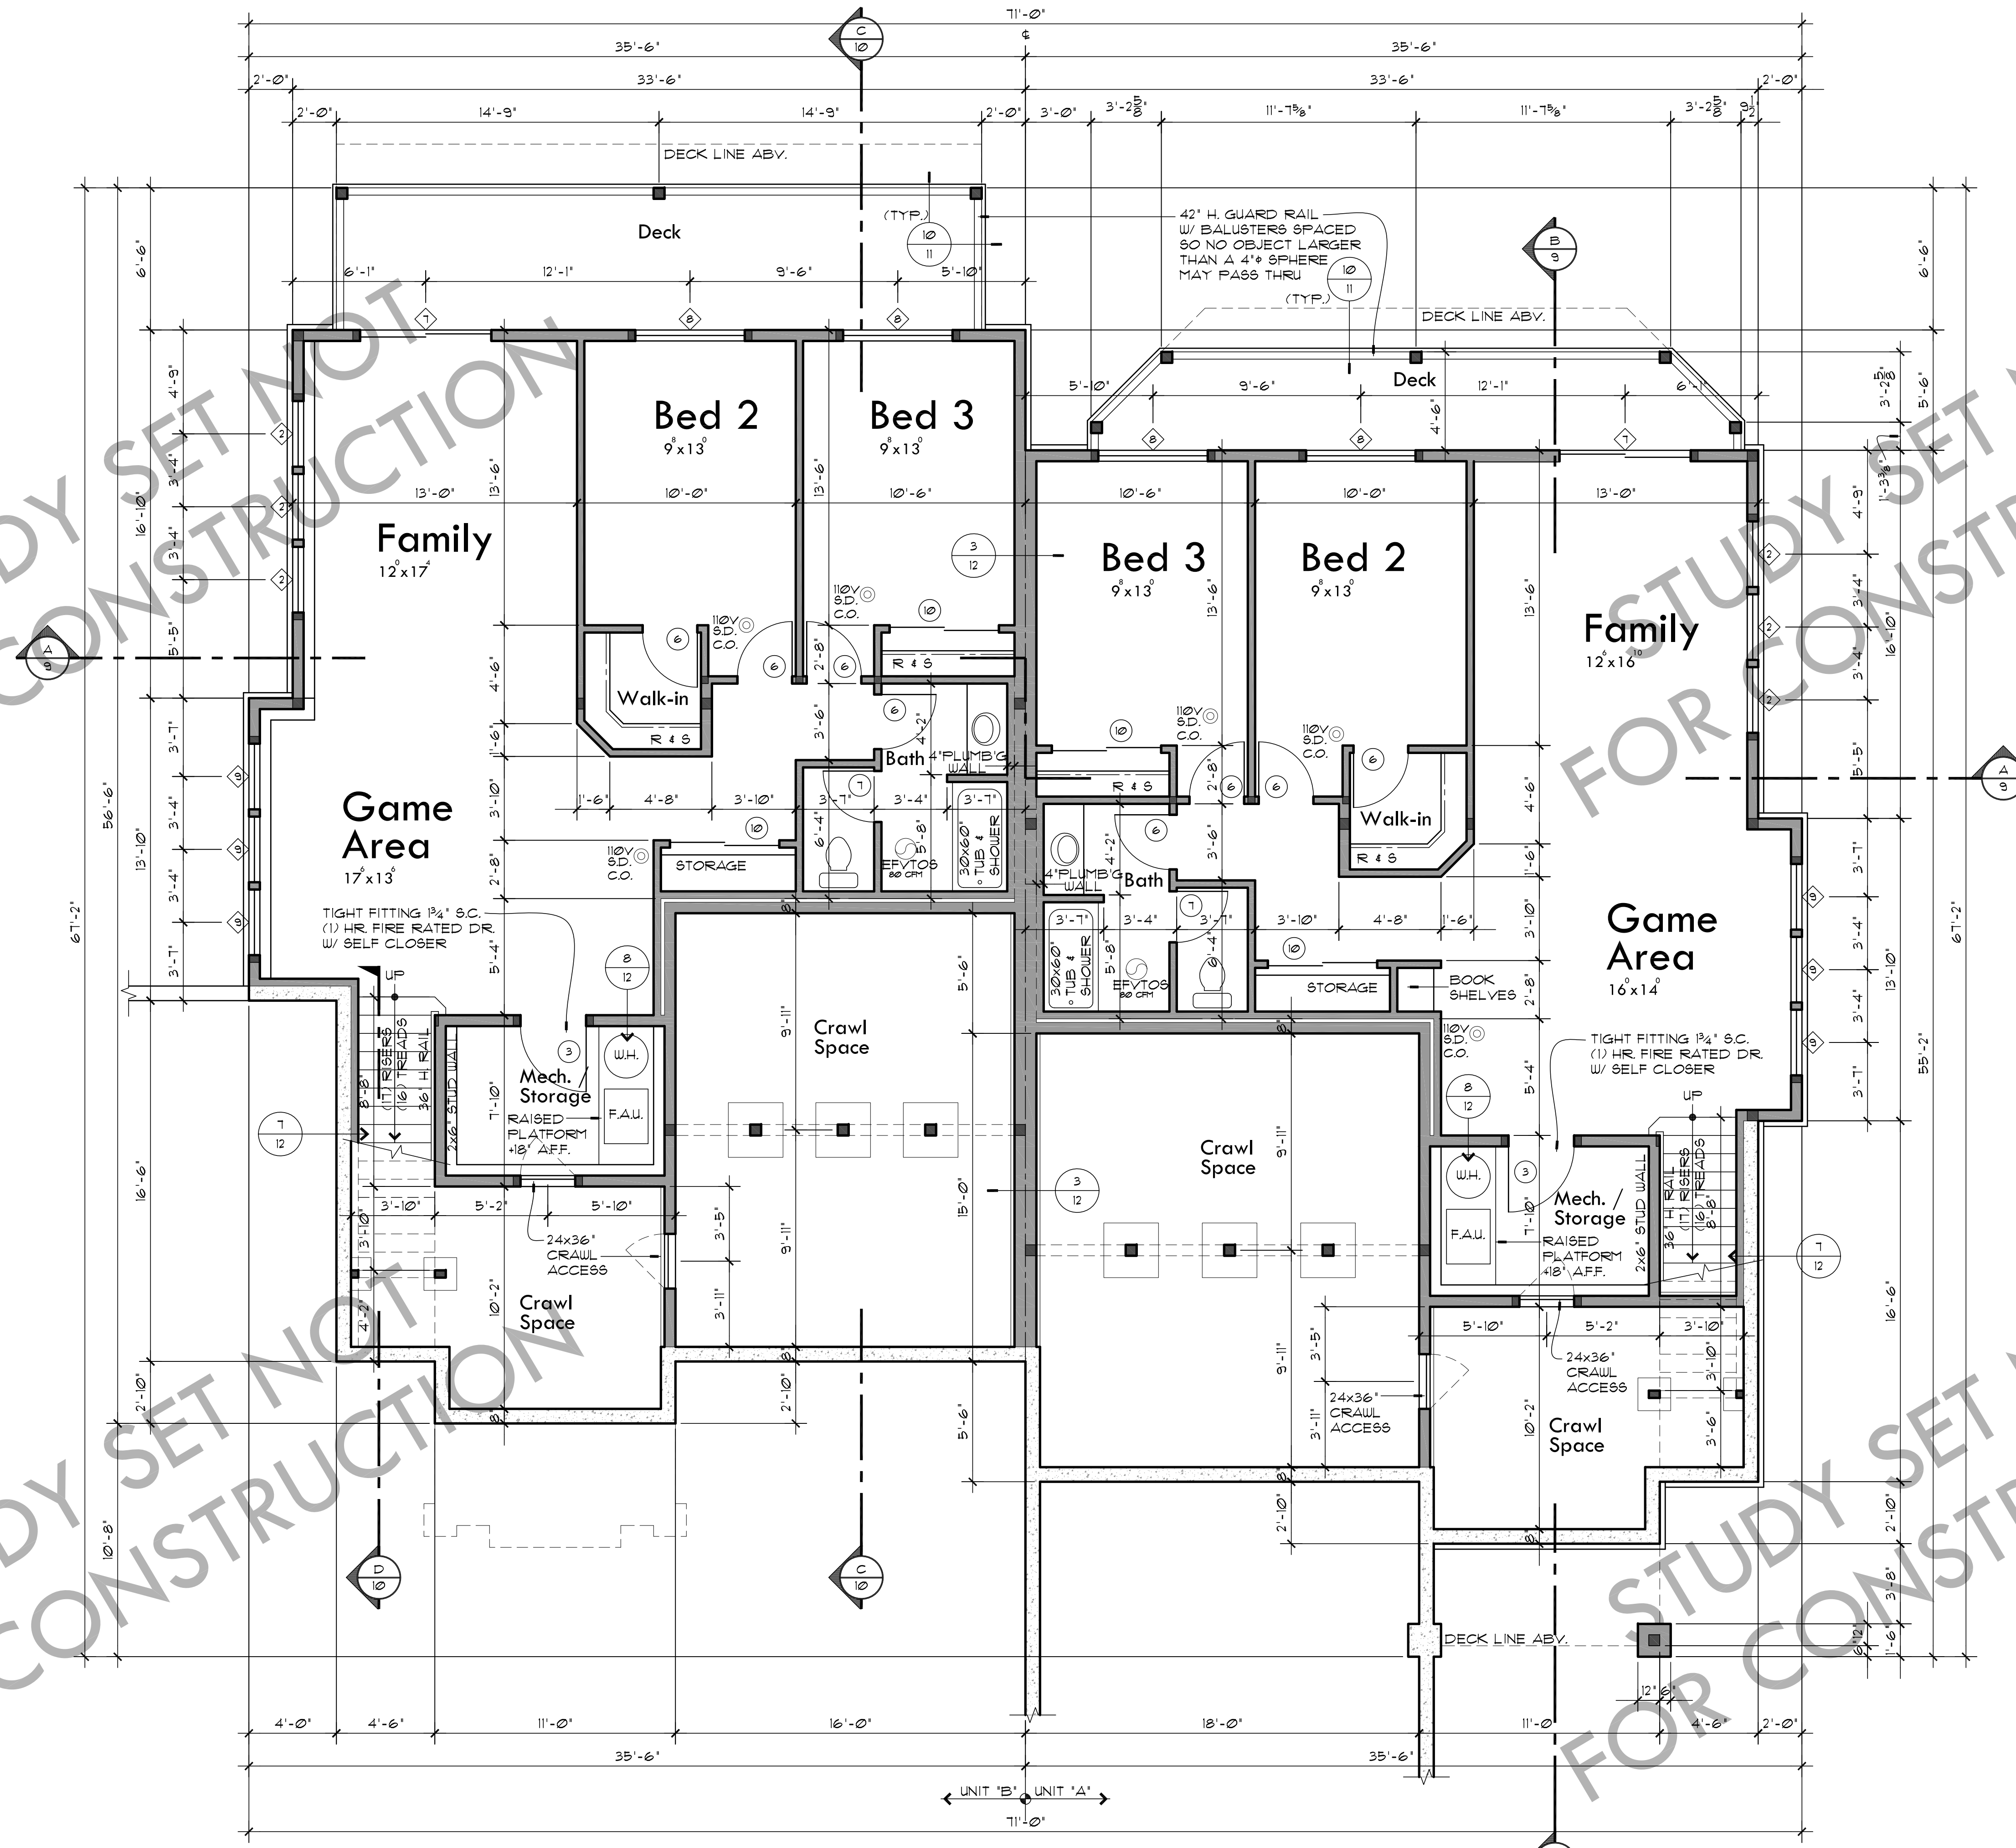

LOWER FLOOR PLAN

SCALE: 1/4"=1'-0"

NOTE:
REFER TO ENGINEERING SHEETS L1 THRU L3 FOR
ADDITIONAL INFORMATION & CALLOUTS

SQUARE FOOTAGE UNIT 'A'	
MAIN FLOOR:	1270#
LOWER FLOOR:	1079#
TOTAL LIVING AREA: 2349#	
GARAGE:	369#
DECK MAIN:	165#
DECK LOWER:	123#
PORCH:	50#

SQUARE FOOTAGE UNIT 'B'	
MAIN FLOOR:	1278#
LOWER FLOOR:	1046#
TOTAL LIVING AREA: 2324#	
GARAGE:	328#
DECK MAIN:	250#
DECK LOWER:	192#
PORCH:	50#

NOTE:
◇ REFER TO WINDOW SCHEDULE
SHEET #10
● REFER TO DOOR SCHEDULE
SHEET #10

These plans are limited to one construction only by the purchaser. The reseller, or reproduction, of these plans without the written consent of the publisher is strictly prohibited by law, under the FEDERAL COPYRIGHT ACT TITLE XVII.

WRITTEN DIMENSIONS ON THESE DRAWINGS SHALL HAVE PRECEDENCE OVER SCALED DIMENSIONS. ANY DISCREPANCY BETWEEN THE TWO SHALL BE NOTICED BY THE PURCHASER. ANY VARIATIONS FROM THE CONDITIONS ON THE JOB AND THIS OFFICE MUST BE NOTICED BY THE PURCHASER. ANY VARIATIONS FROM THE DIMENSIONS AND CONDITIONS SHOWN BY THESE DRAWINGS.

houseplans.pro by
Bruinier & associates, inc.
building designers 503-246-3022
1304 SW BERTHA BLVD. PORTLAND OREGON 97219

REVISIONS	CFB	DAW	DATE

SHEET	5	OF	12
PLAN NUMBER	D-511		